




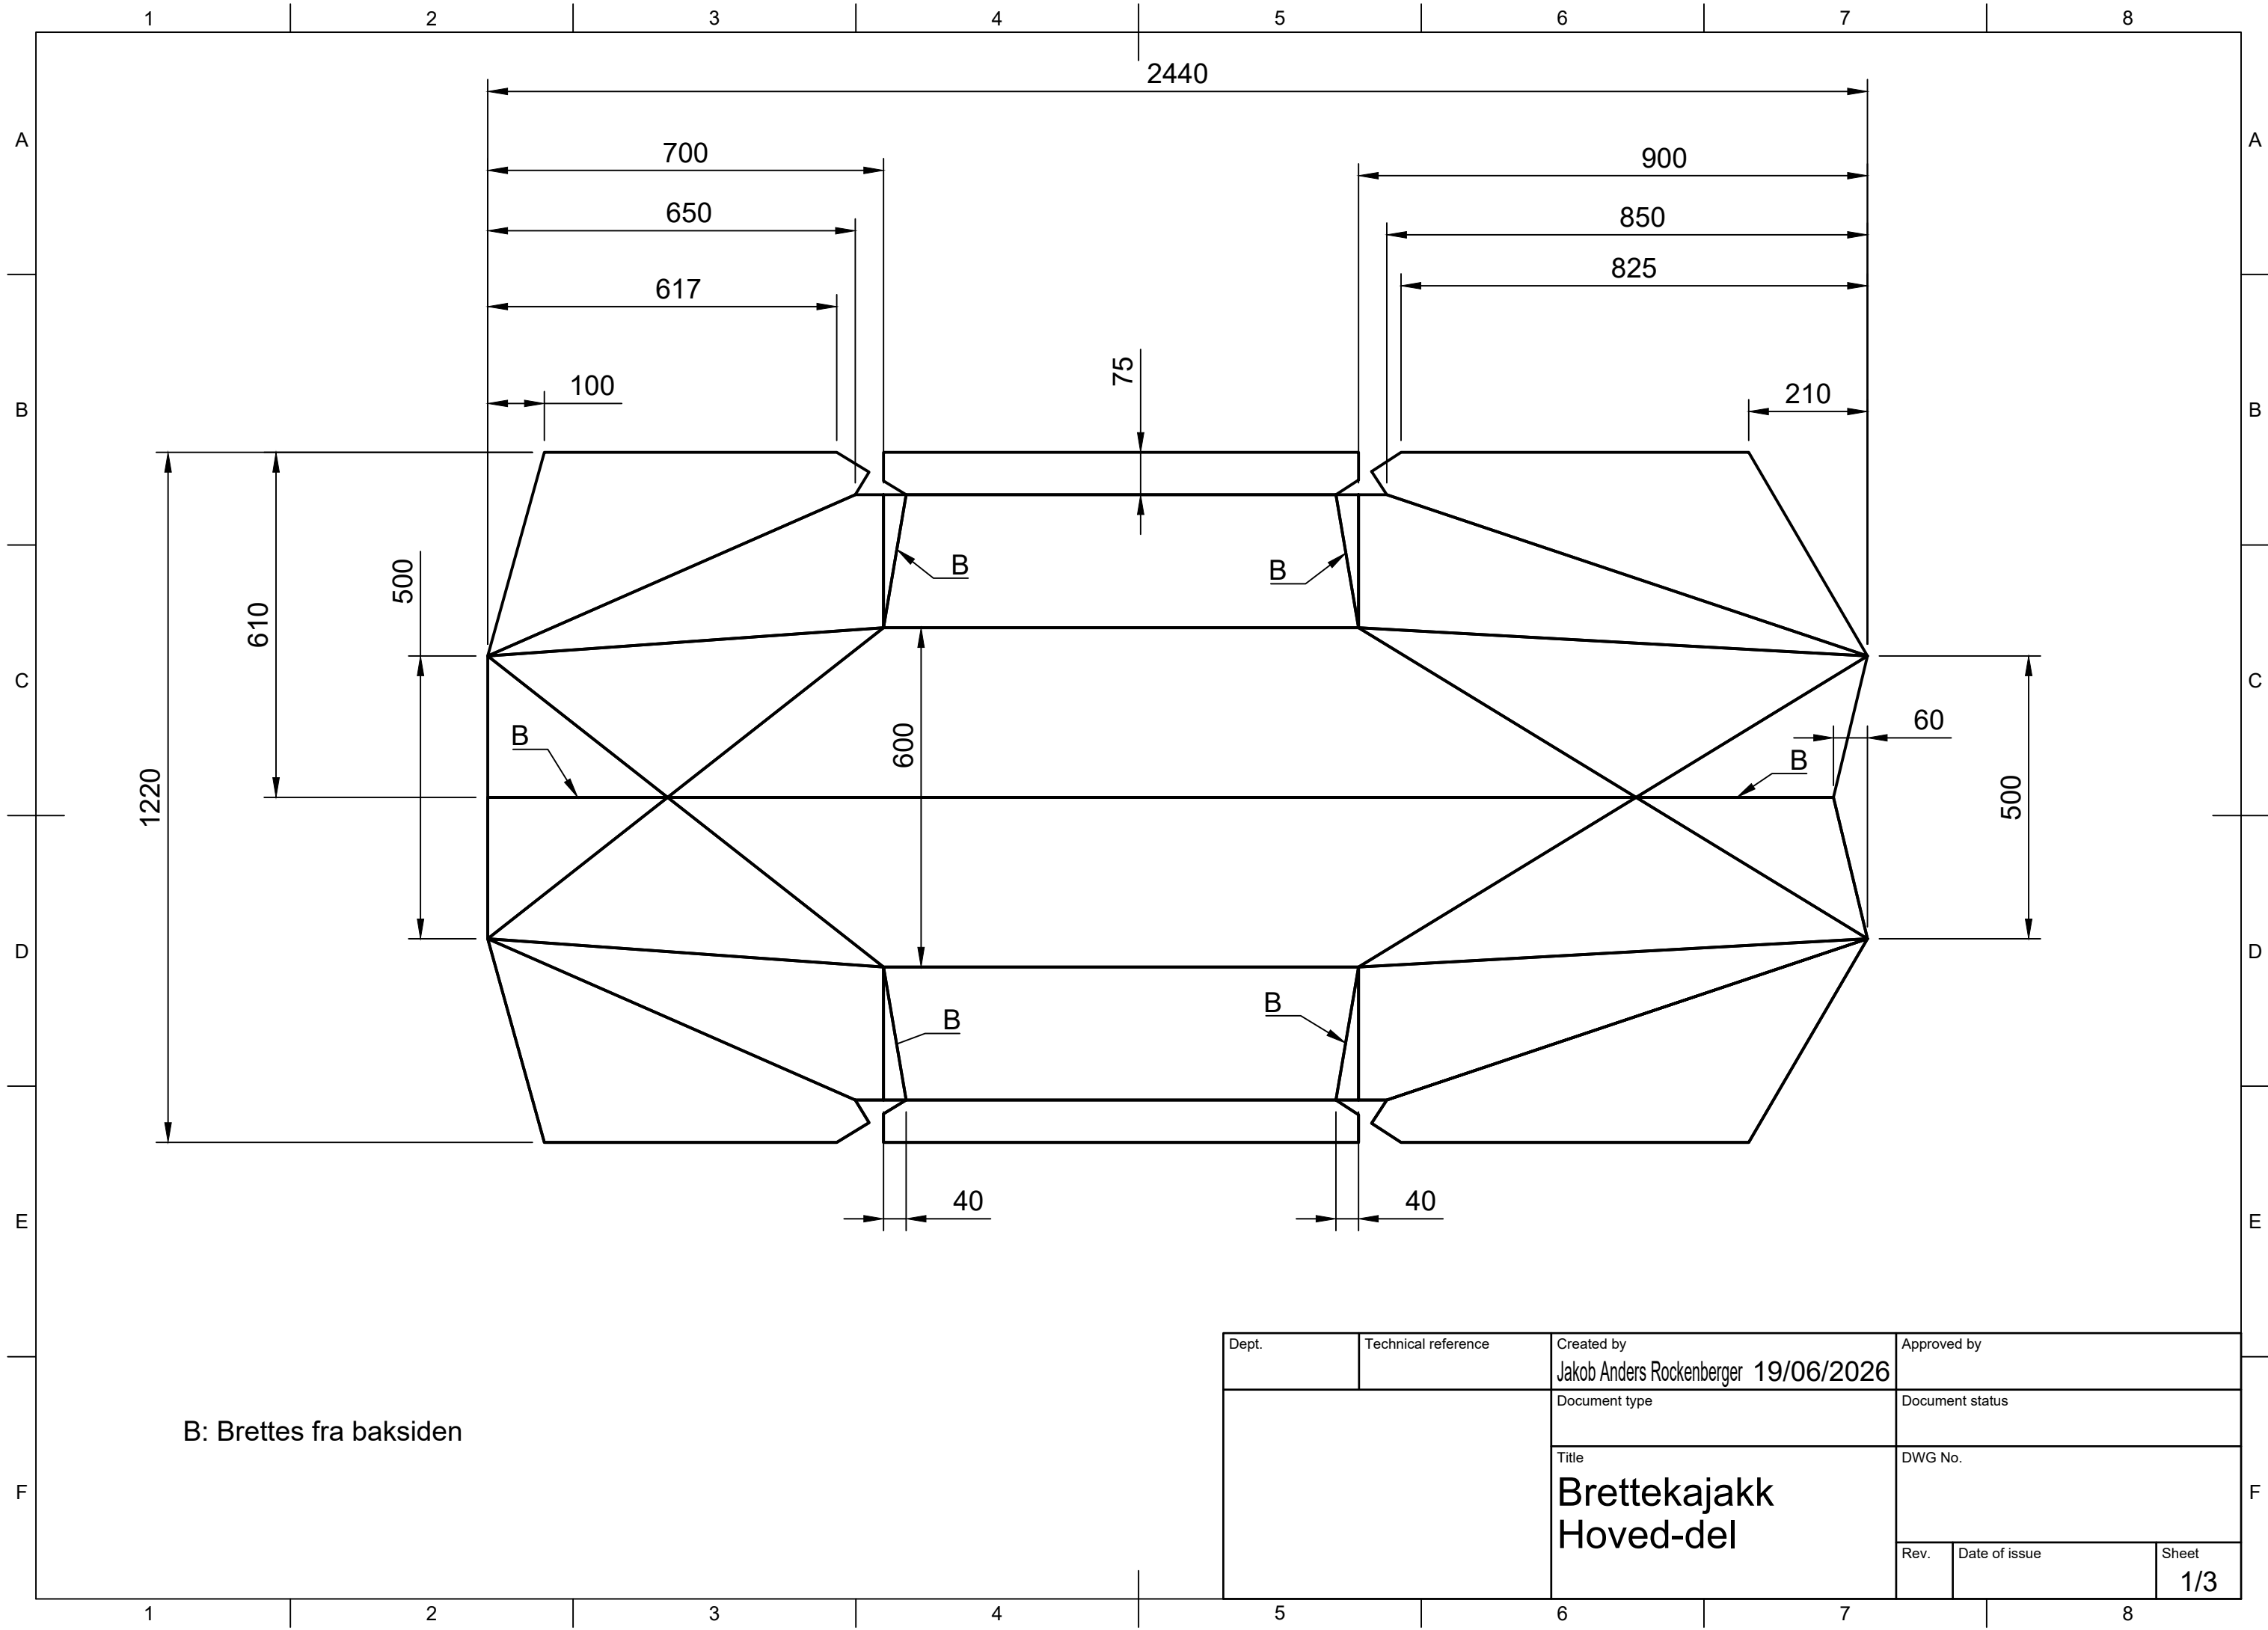

B: Brettes fra baksiden

Dept.	Technical reference	Created by Jakob Anders Rockenberger 19/06/2026	Approved by
		Document type	Document status
		Title Brettekajakk Hoved-del	DWG No.
		Rev.	Date of issue
		Sheet 1/3	

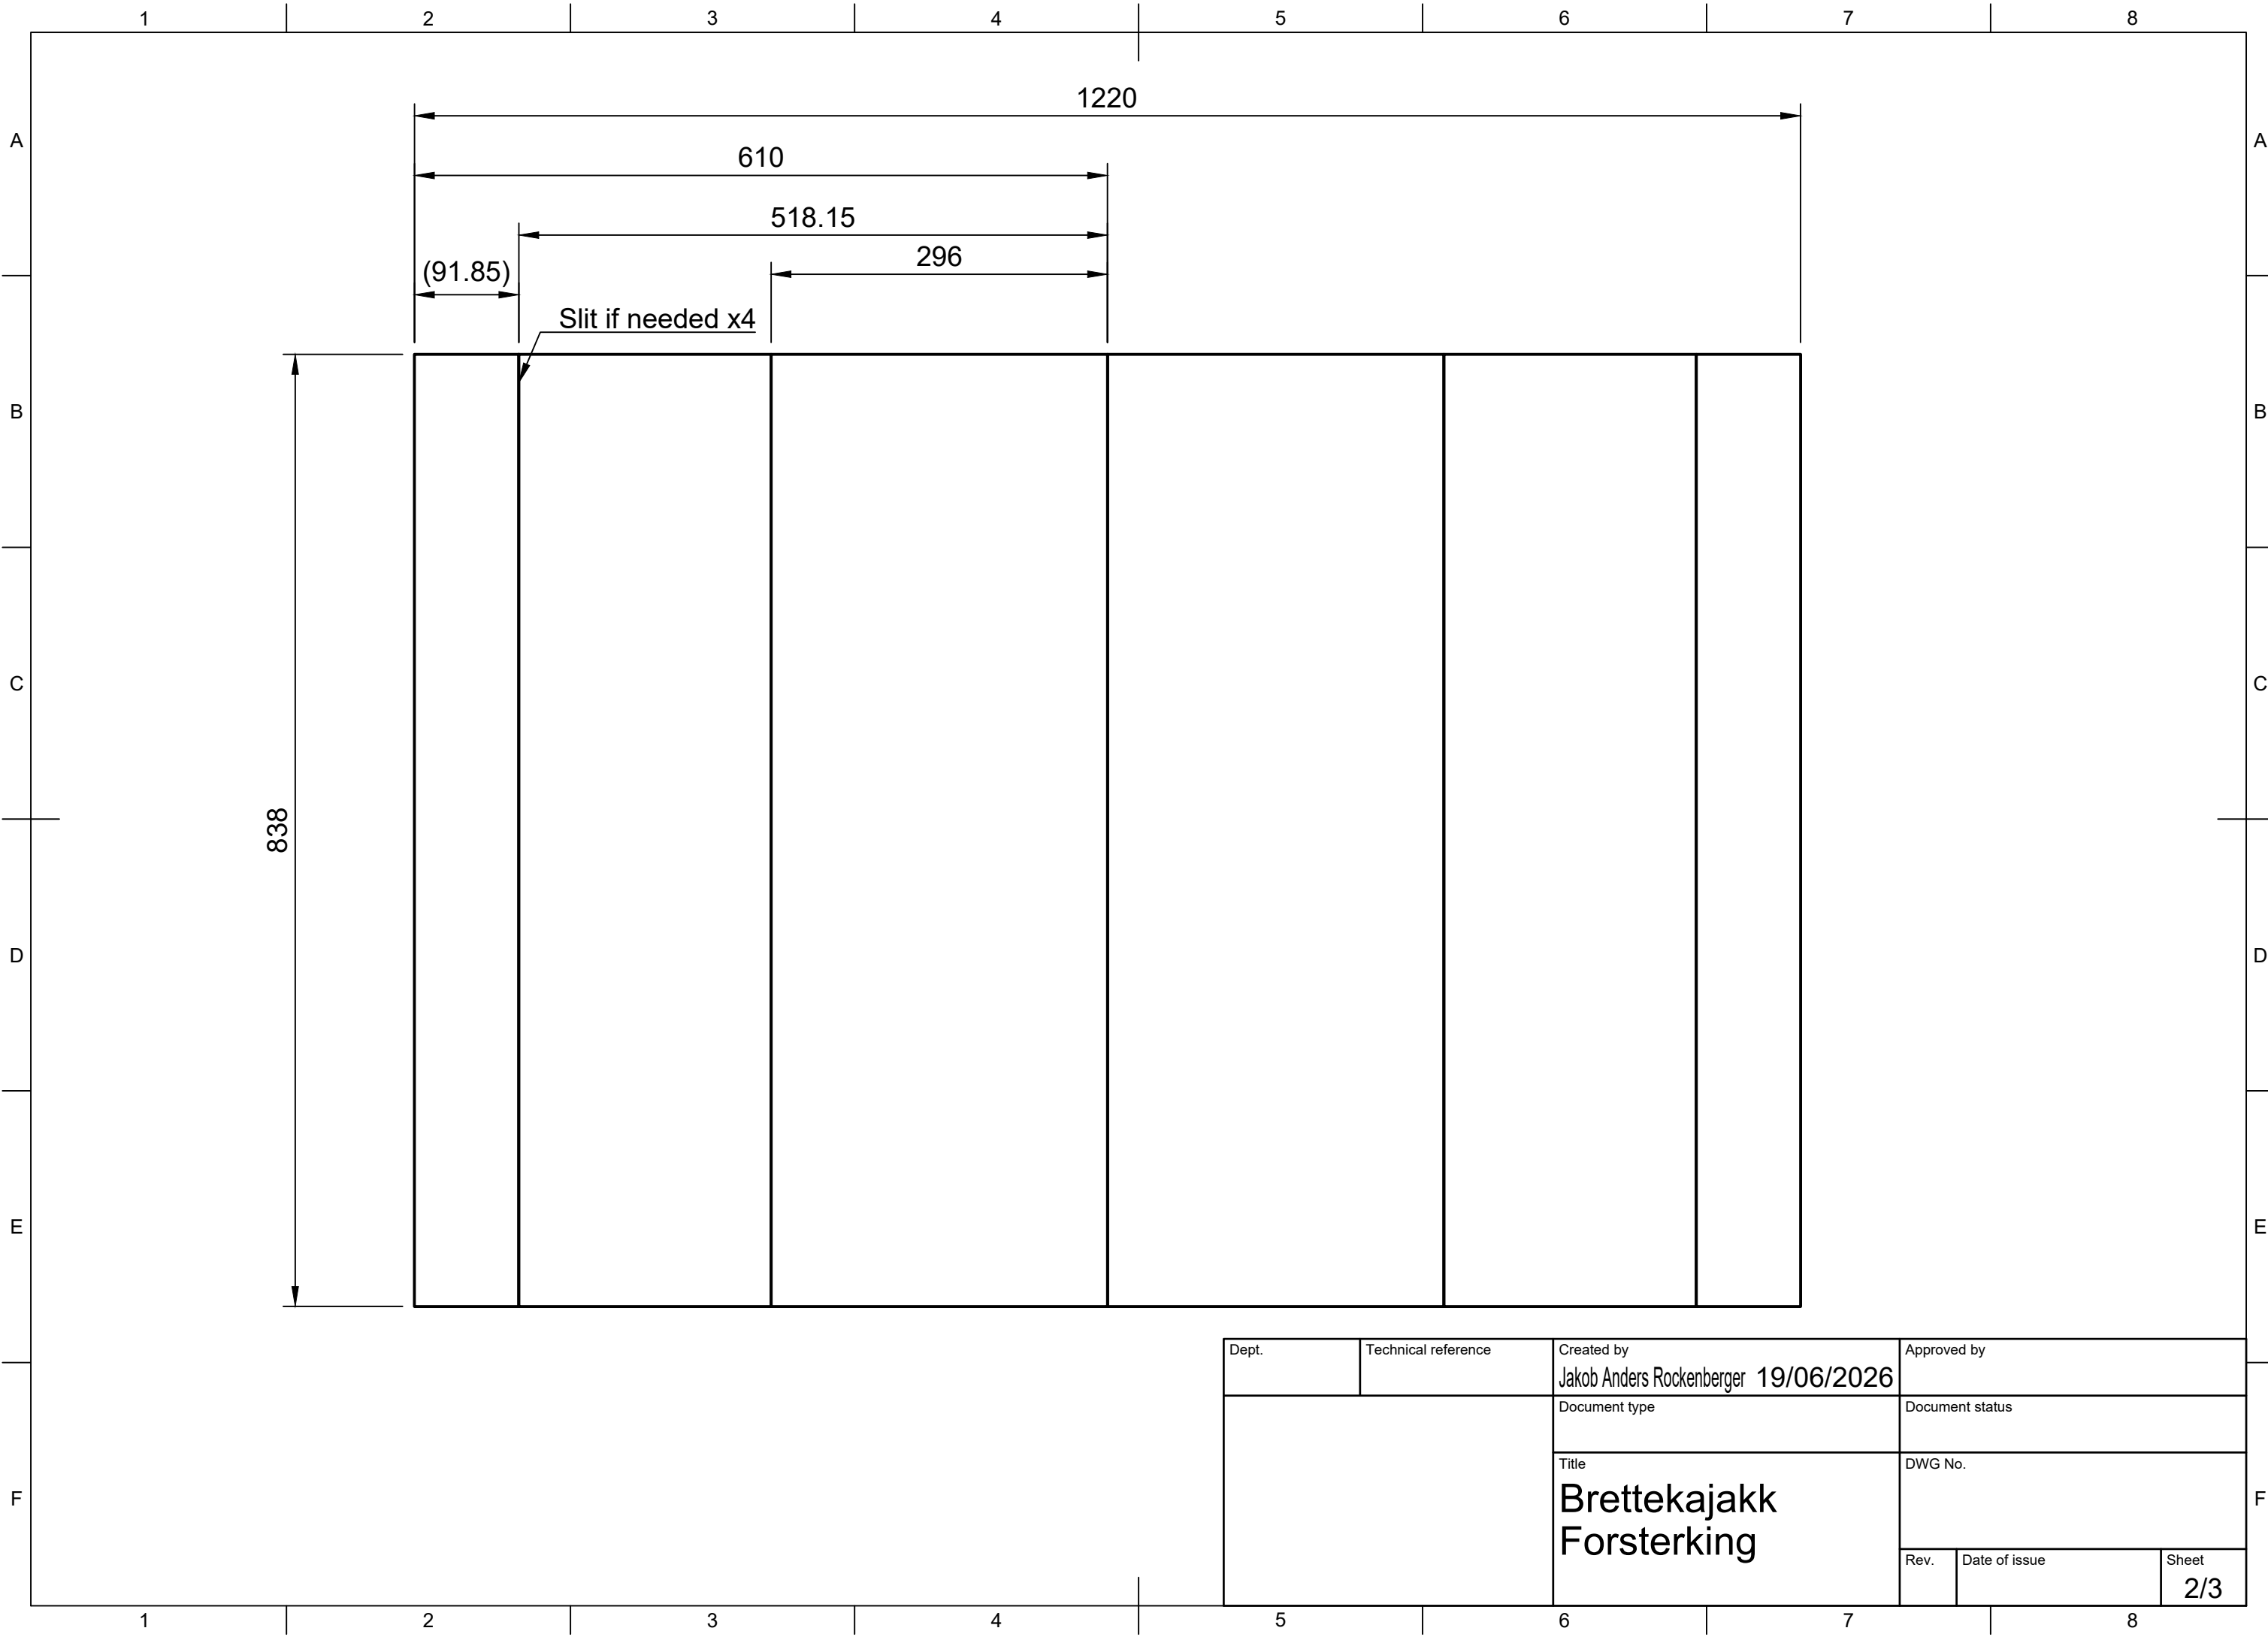

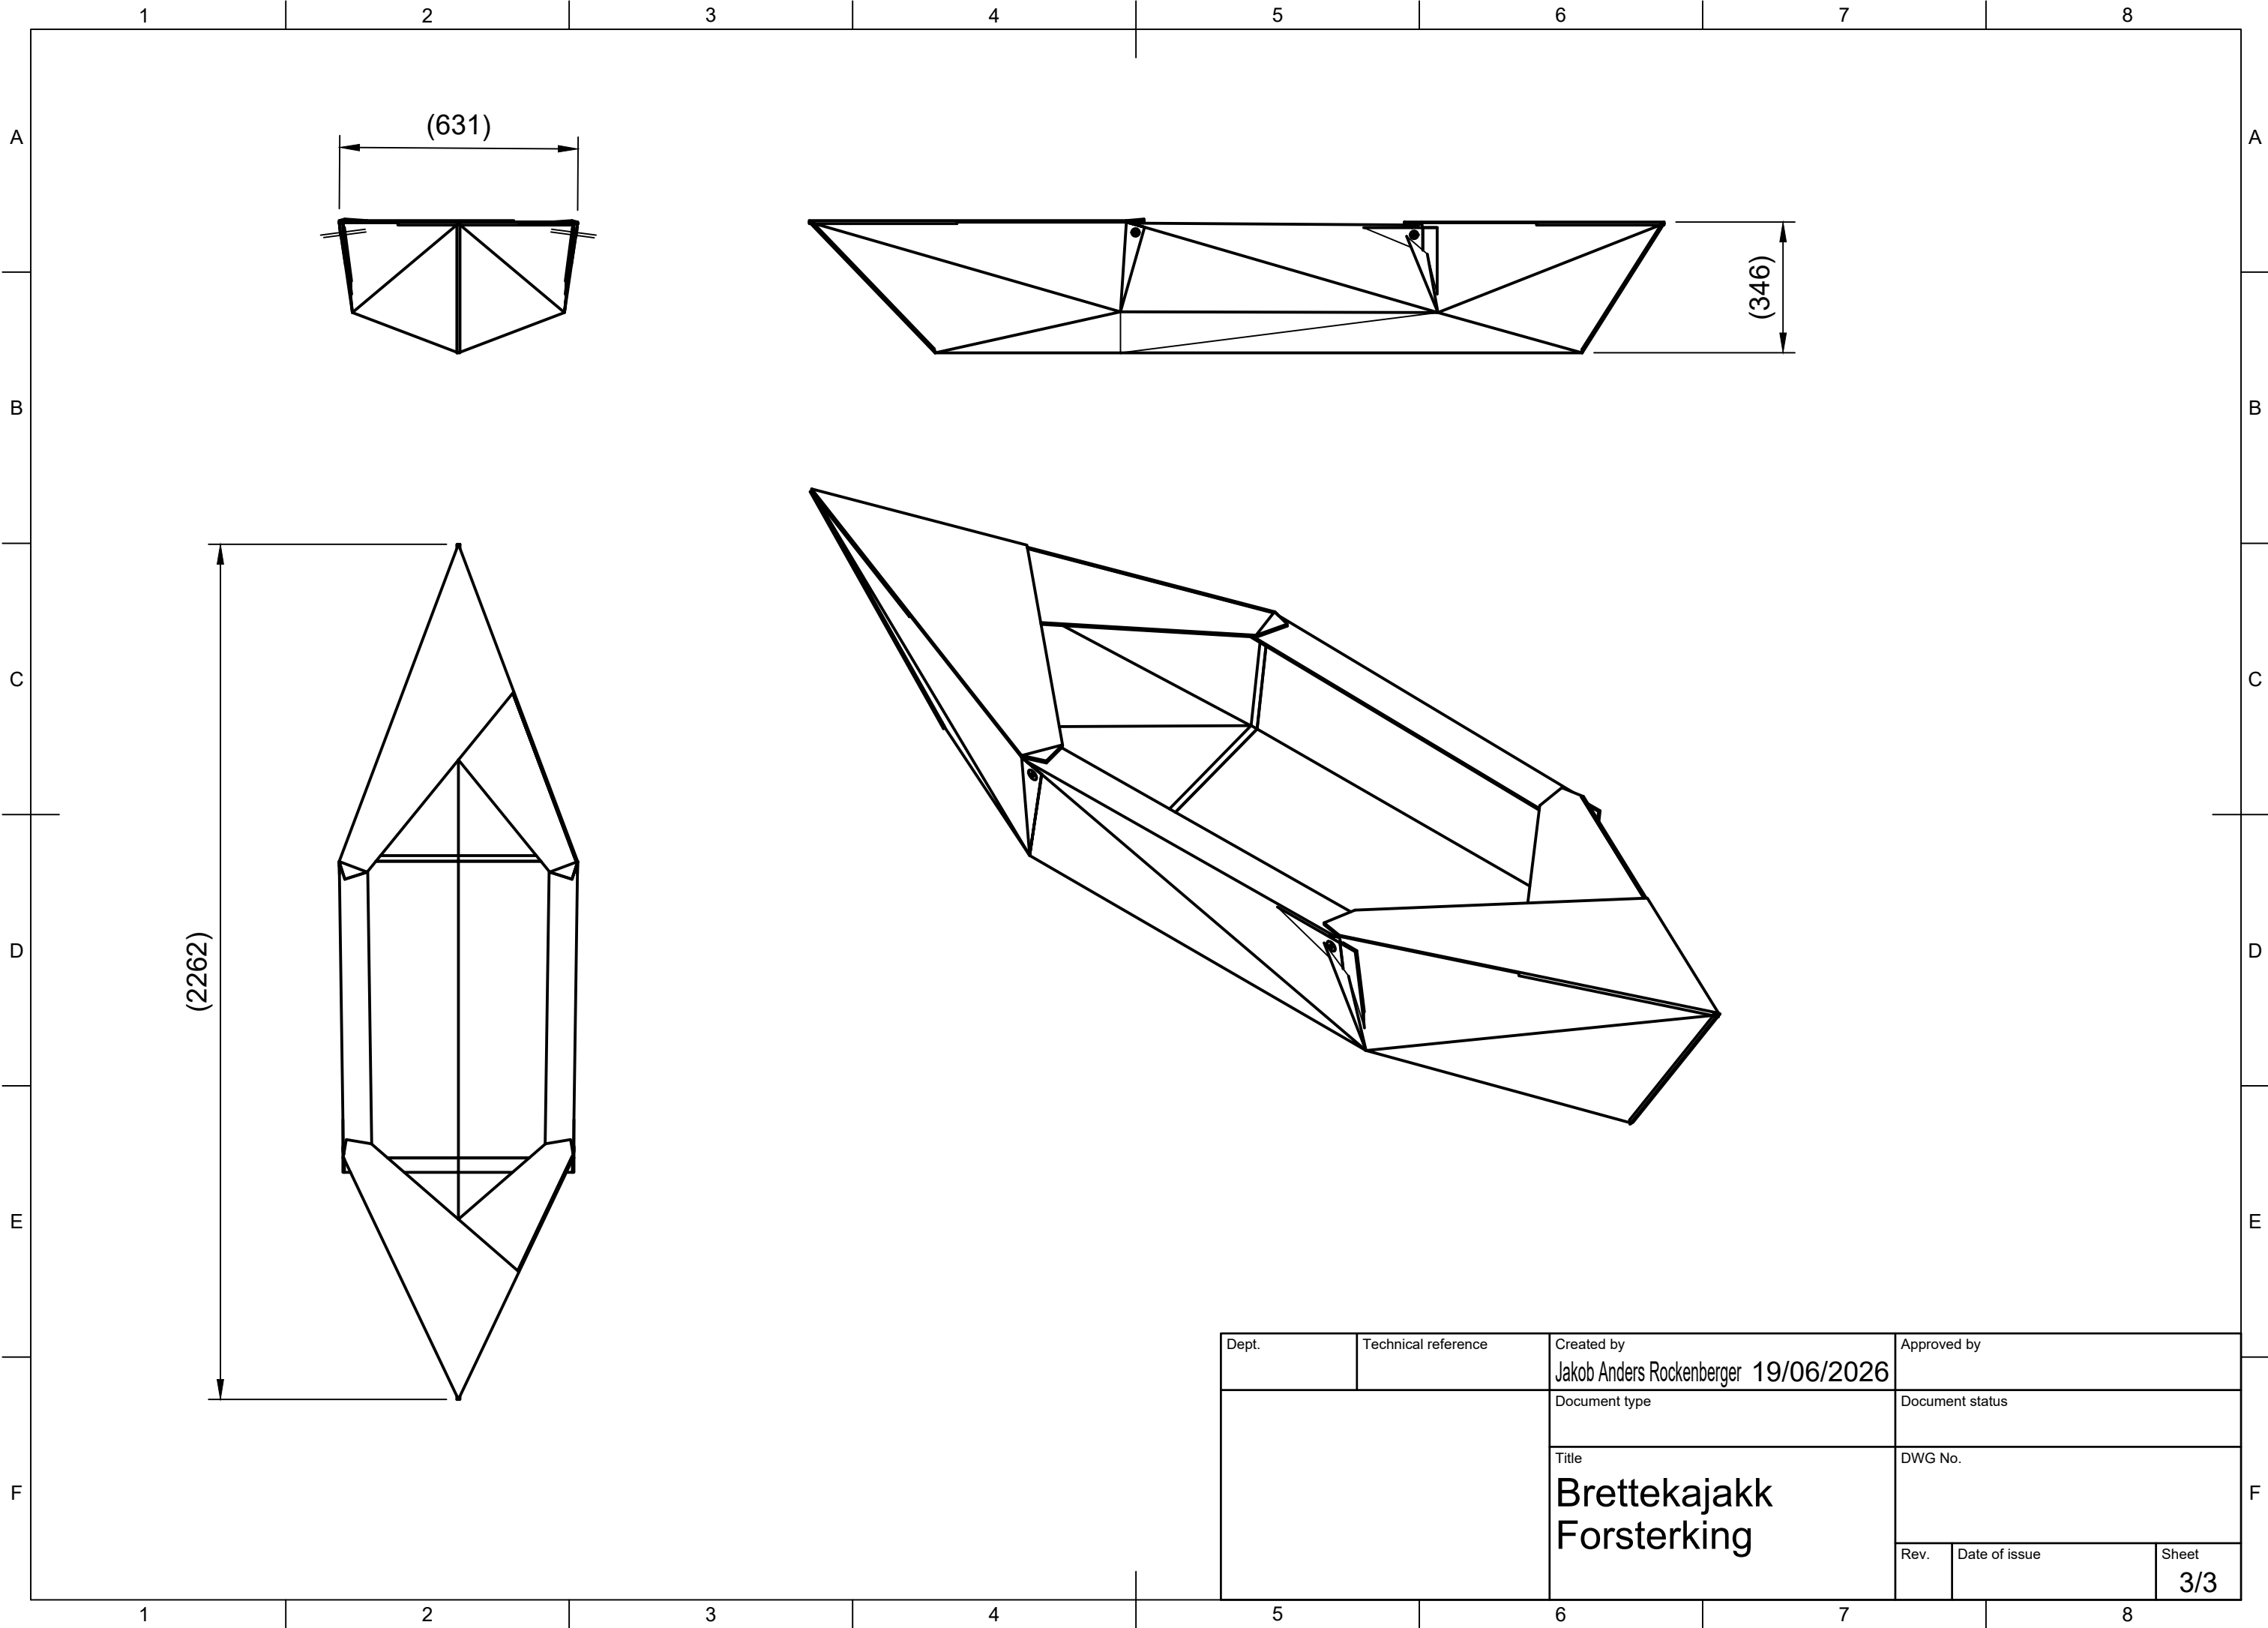

Dept.	Technical reference	Created by Jakob Anders Rockenberger 19/06/2026	Approved by	
			Document status	
			DWG No.	
			Rev.	Date of issue
			Sheet 3/3	